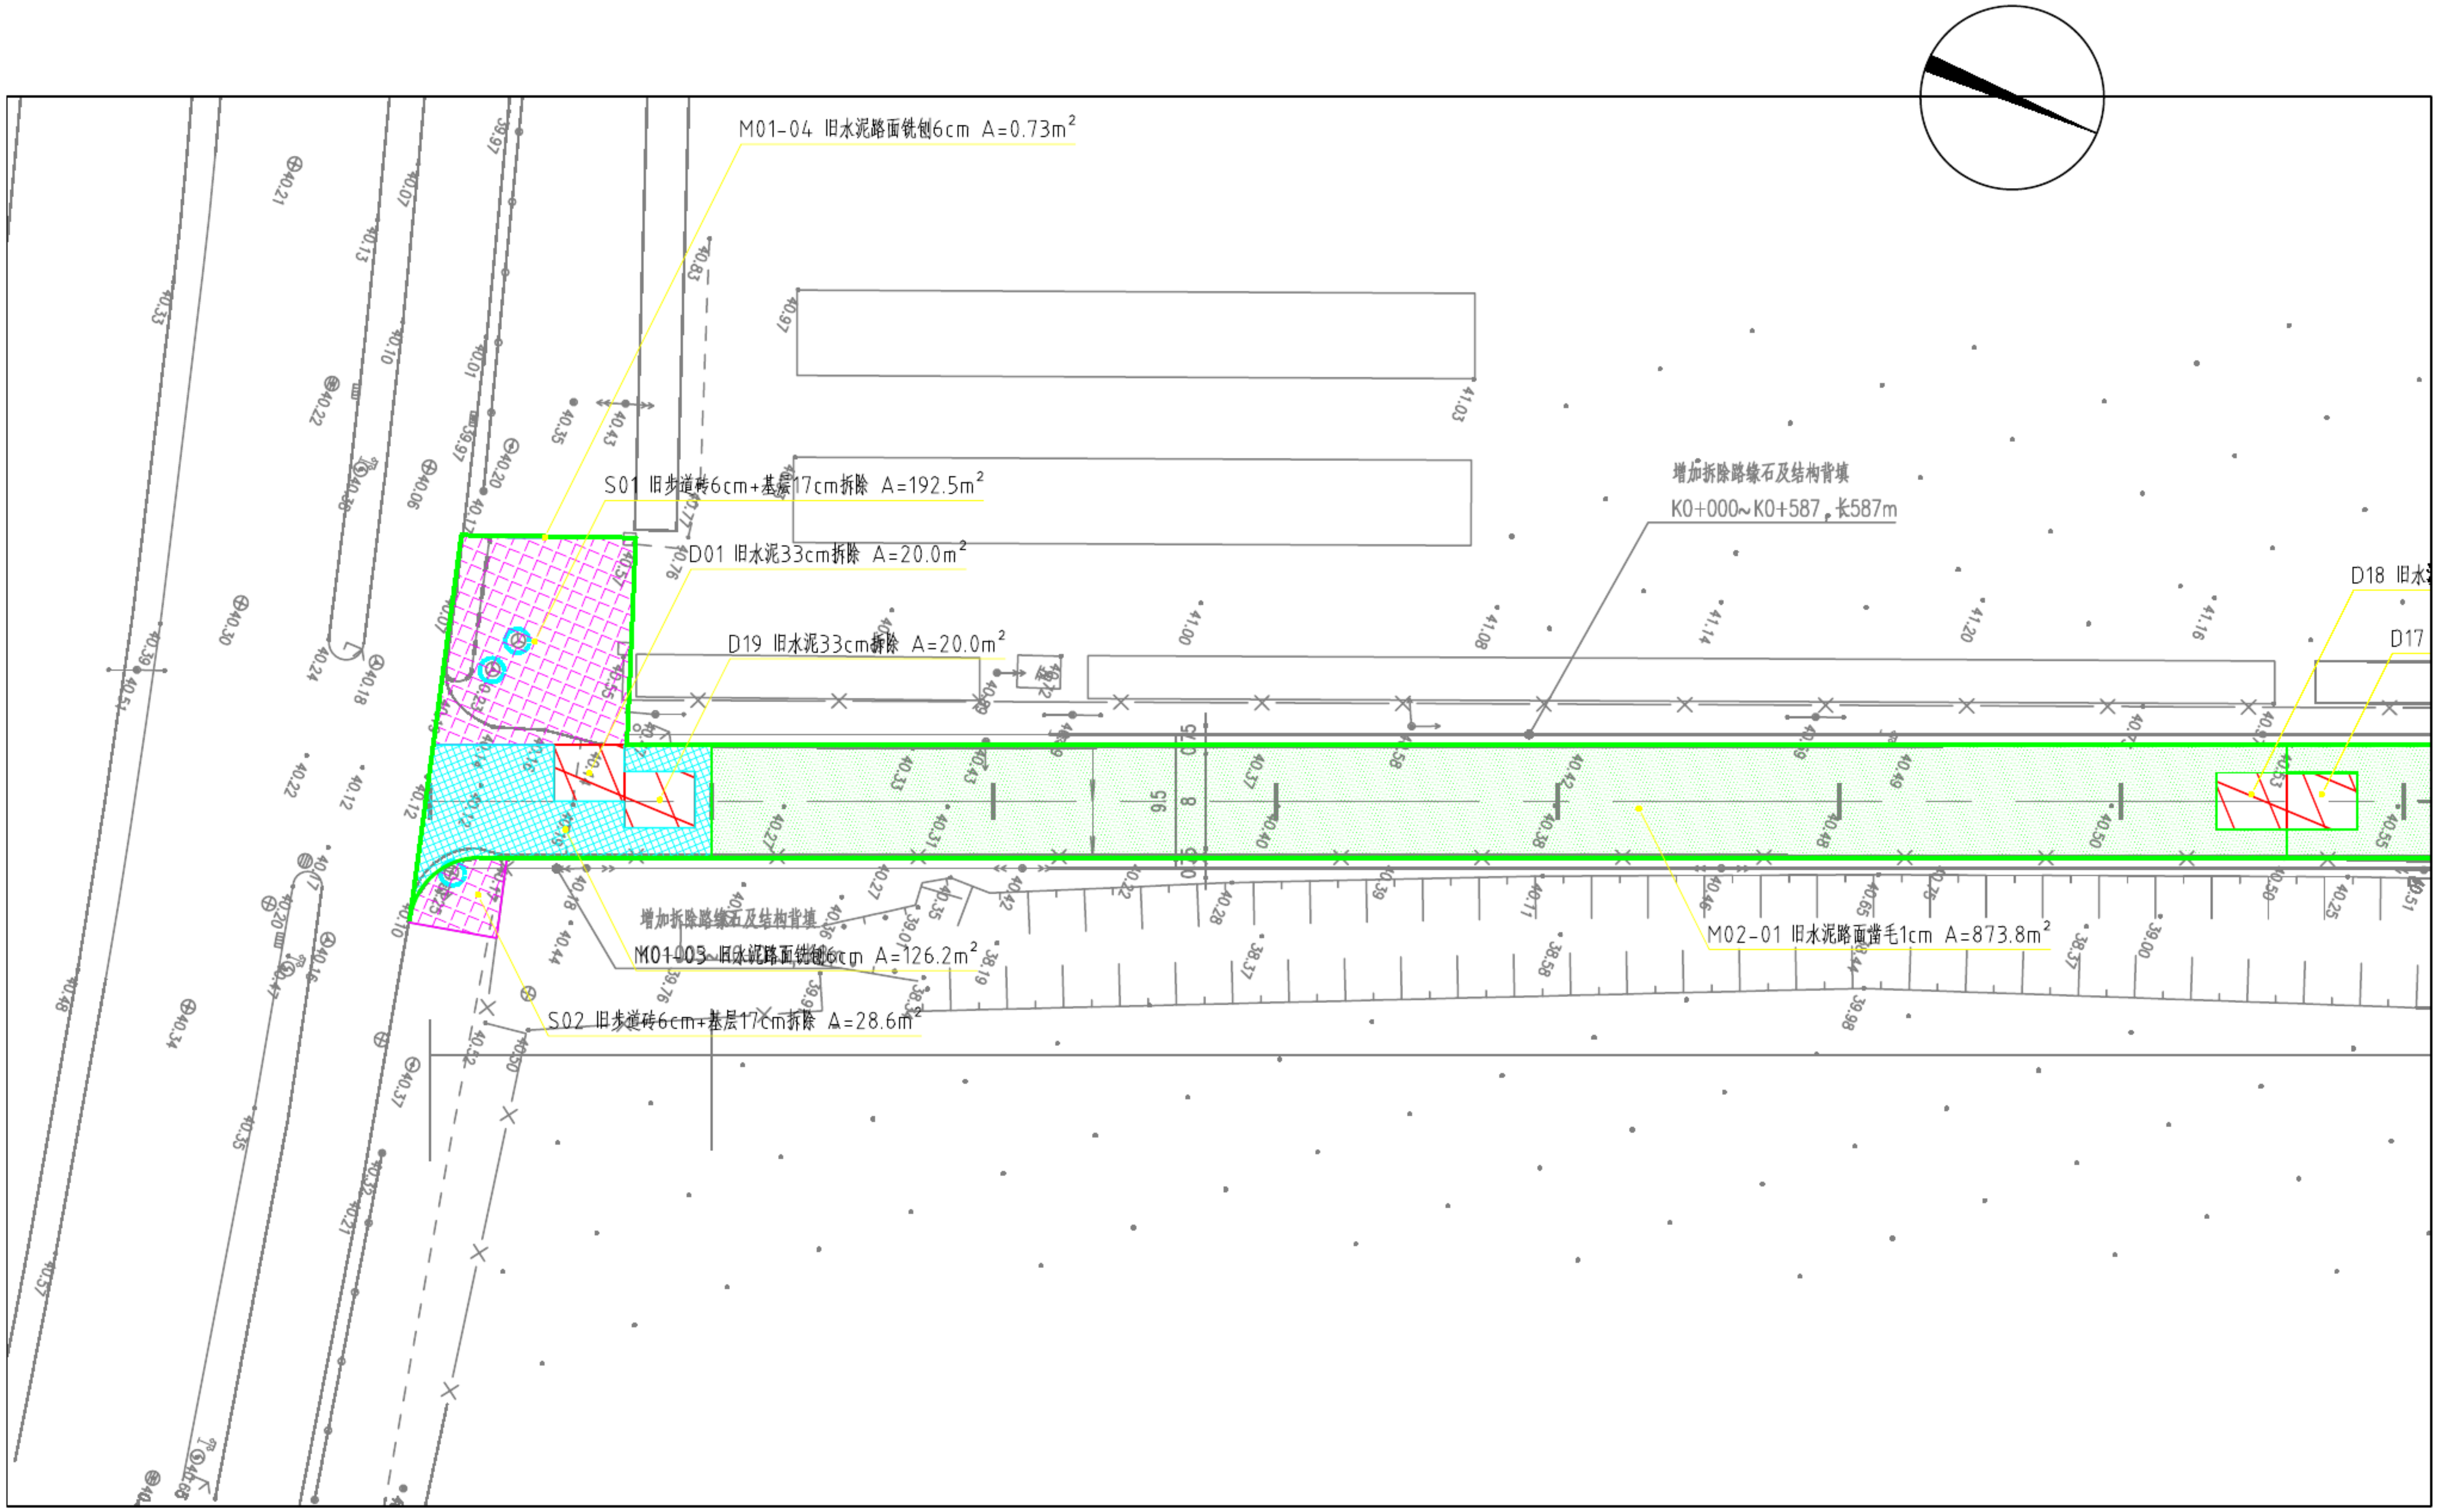
M01-04 旧水泥路面铣刨6cm A=0.73m²
S01 旧步道砖6cm+基层17cm拆除 A=192.5m²
D01 旧水泥33cm拆除 A=20.0m²
D19 旧水泥33cm拆除 A=20.0m²
增加拆除路缘石及结构背填
K0+000~K0+587，长587m
D18 旧水
D17
9.5
8
0.75
0.75
增加拆除路缘石及结构背填
M01-03 旧水泥路面铣刨6cm A=126.2m²
S02 旧步道砖6cm+基层17cm拆除 A=28.6m²
M02-01 旧水泥路面凿毛1cm A=873.8m²

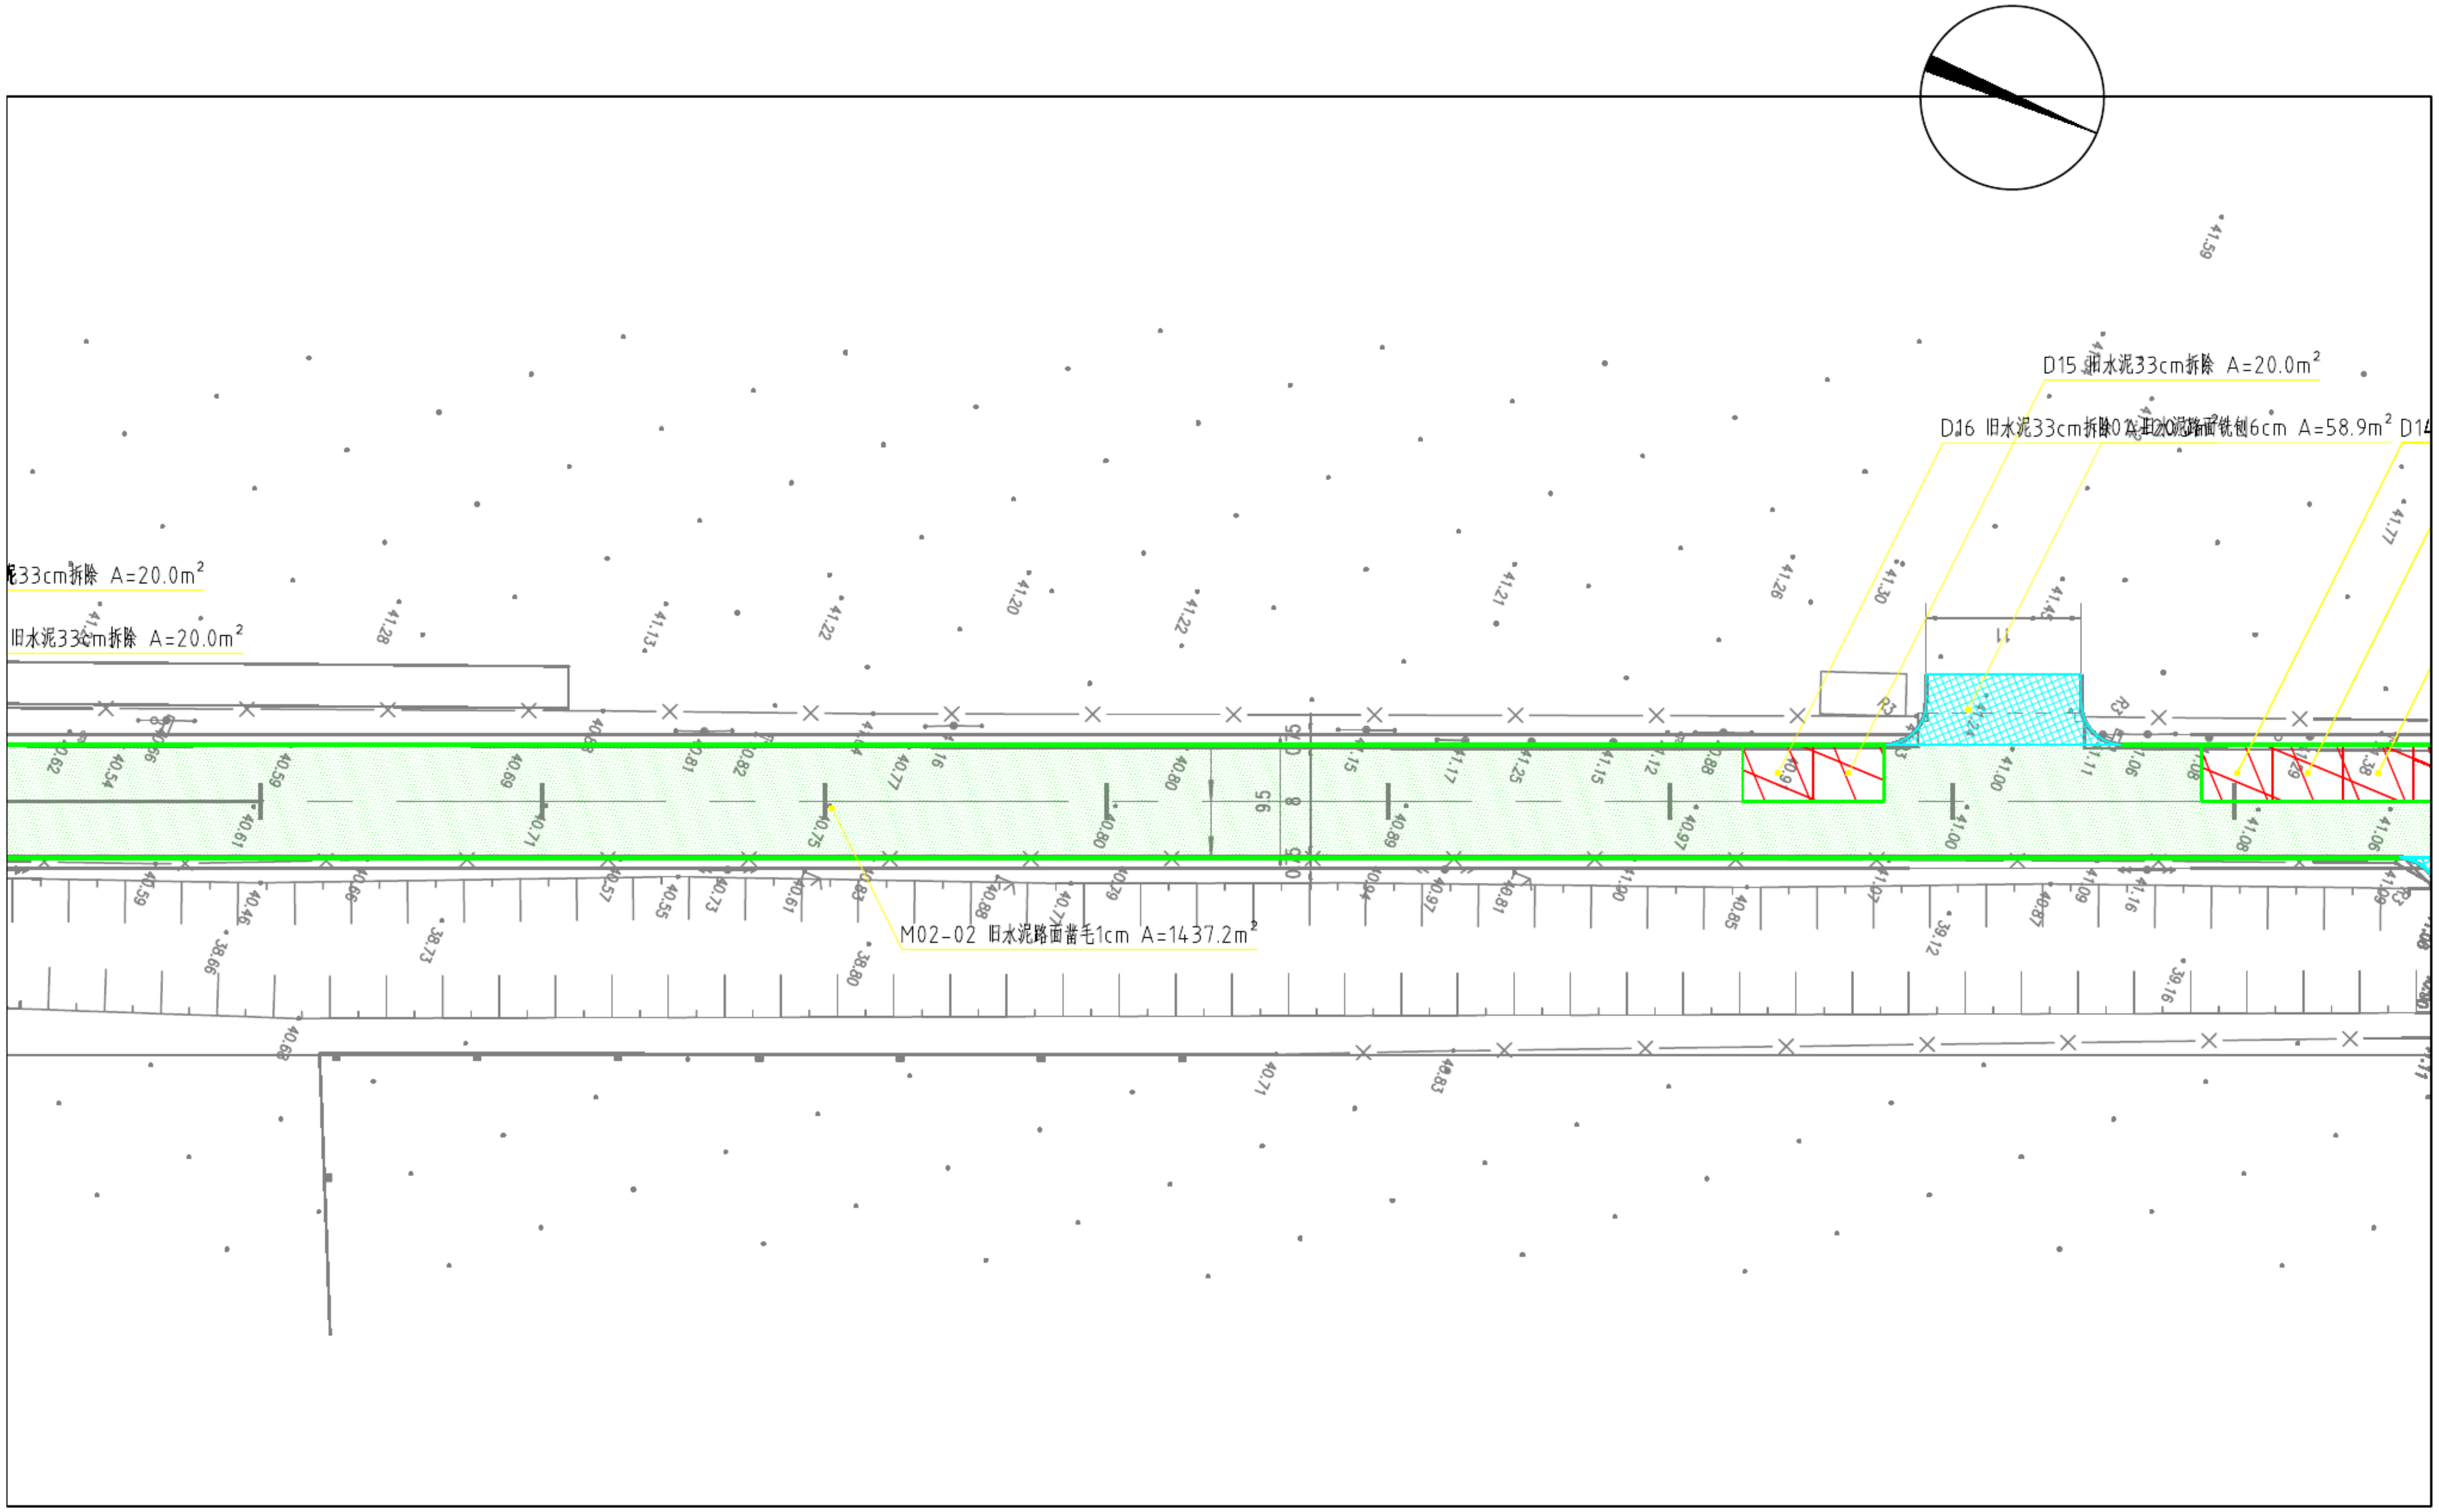D15 旧水泥33cm拆除 A=20.0m²
D16 旧水泥33cm拆除 A=20.0m²
旧水泥路面铣刨6cm A=58.9m²
D14
泥33cm拆除 A=20.0m²
旧水泥33cm拆除 A=20.0m²
M02-02 旧水泥路面凿毛1cm A=1437.2m²
11
95
41.59
41.28
41.13
41.22
41.20
41.22
41.21
41.26
41.30
41.77
40.59
40.69
40.80
40.61
40.71
40.75
40.80
40.89
40.97
41.00
41.08
41.06
38.66
38.73
38.80
39.12
39.16
40.69
40.71
40.83

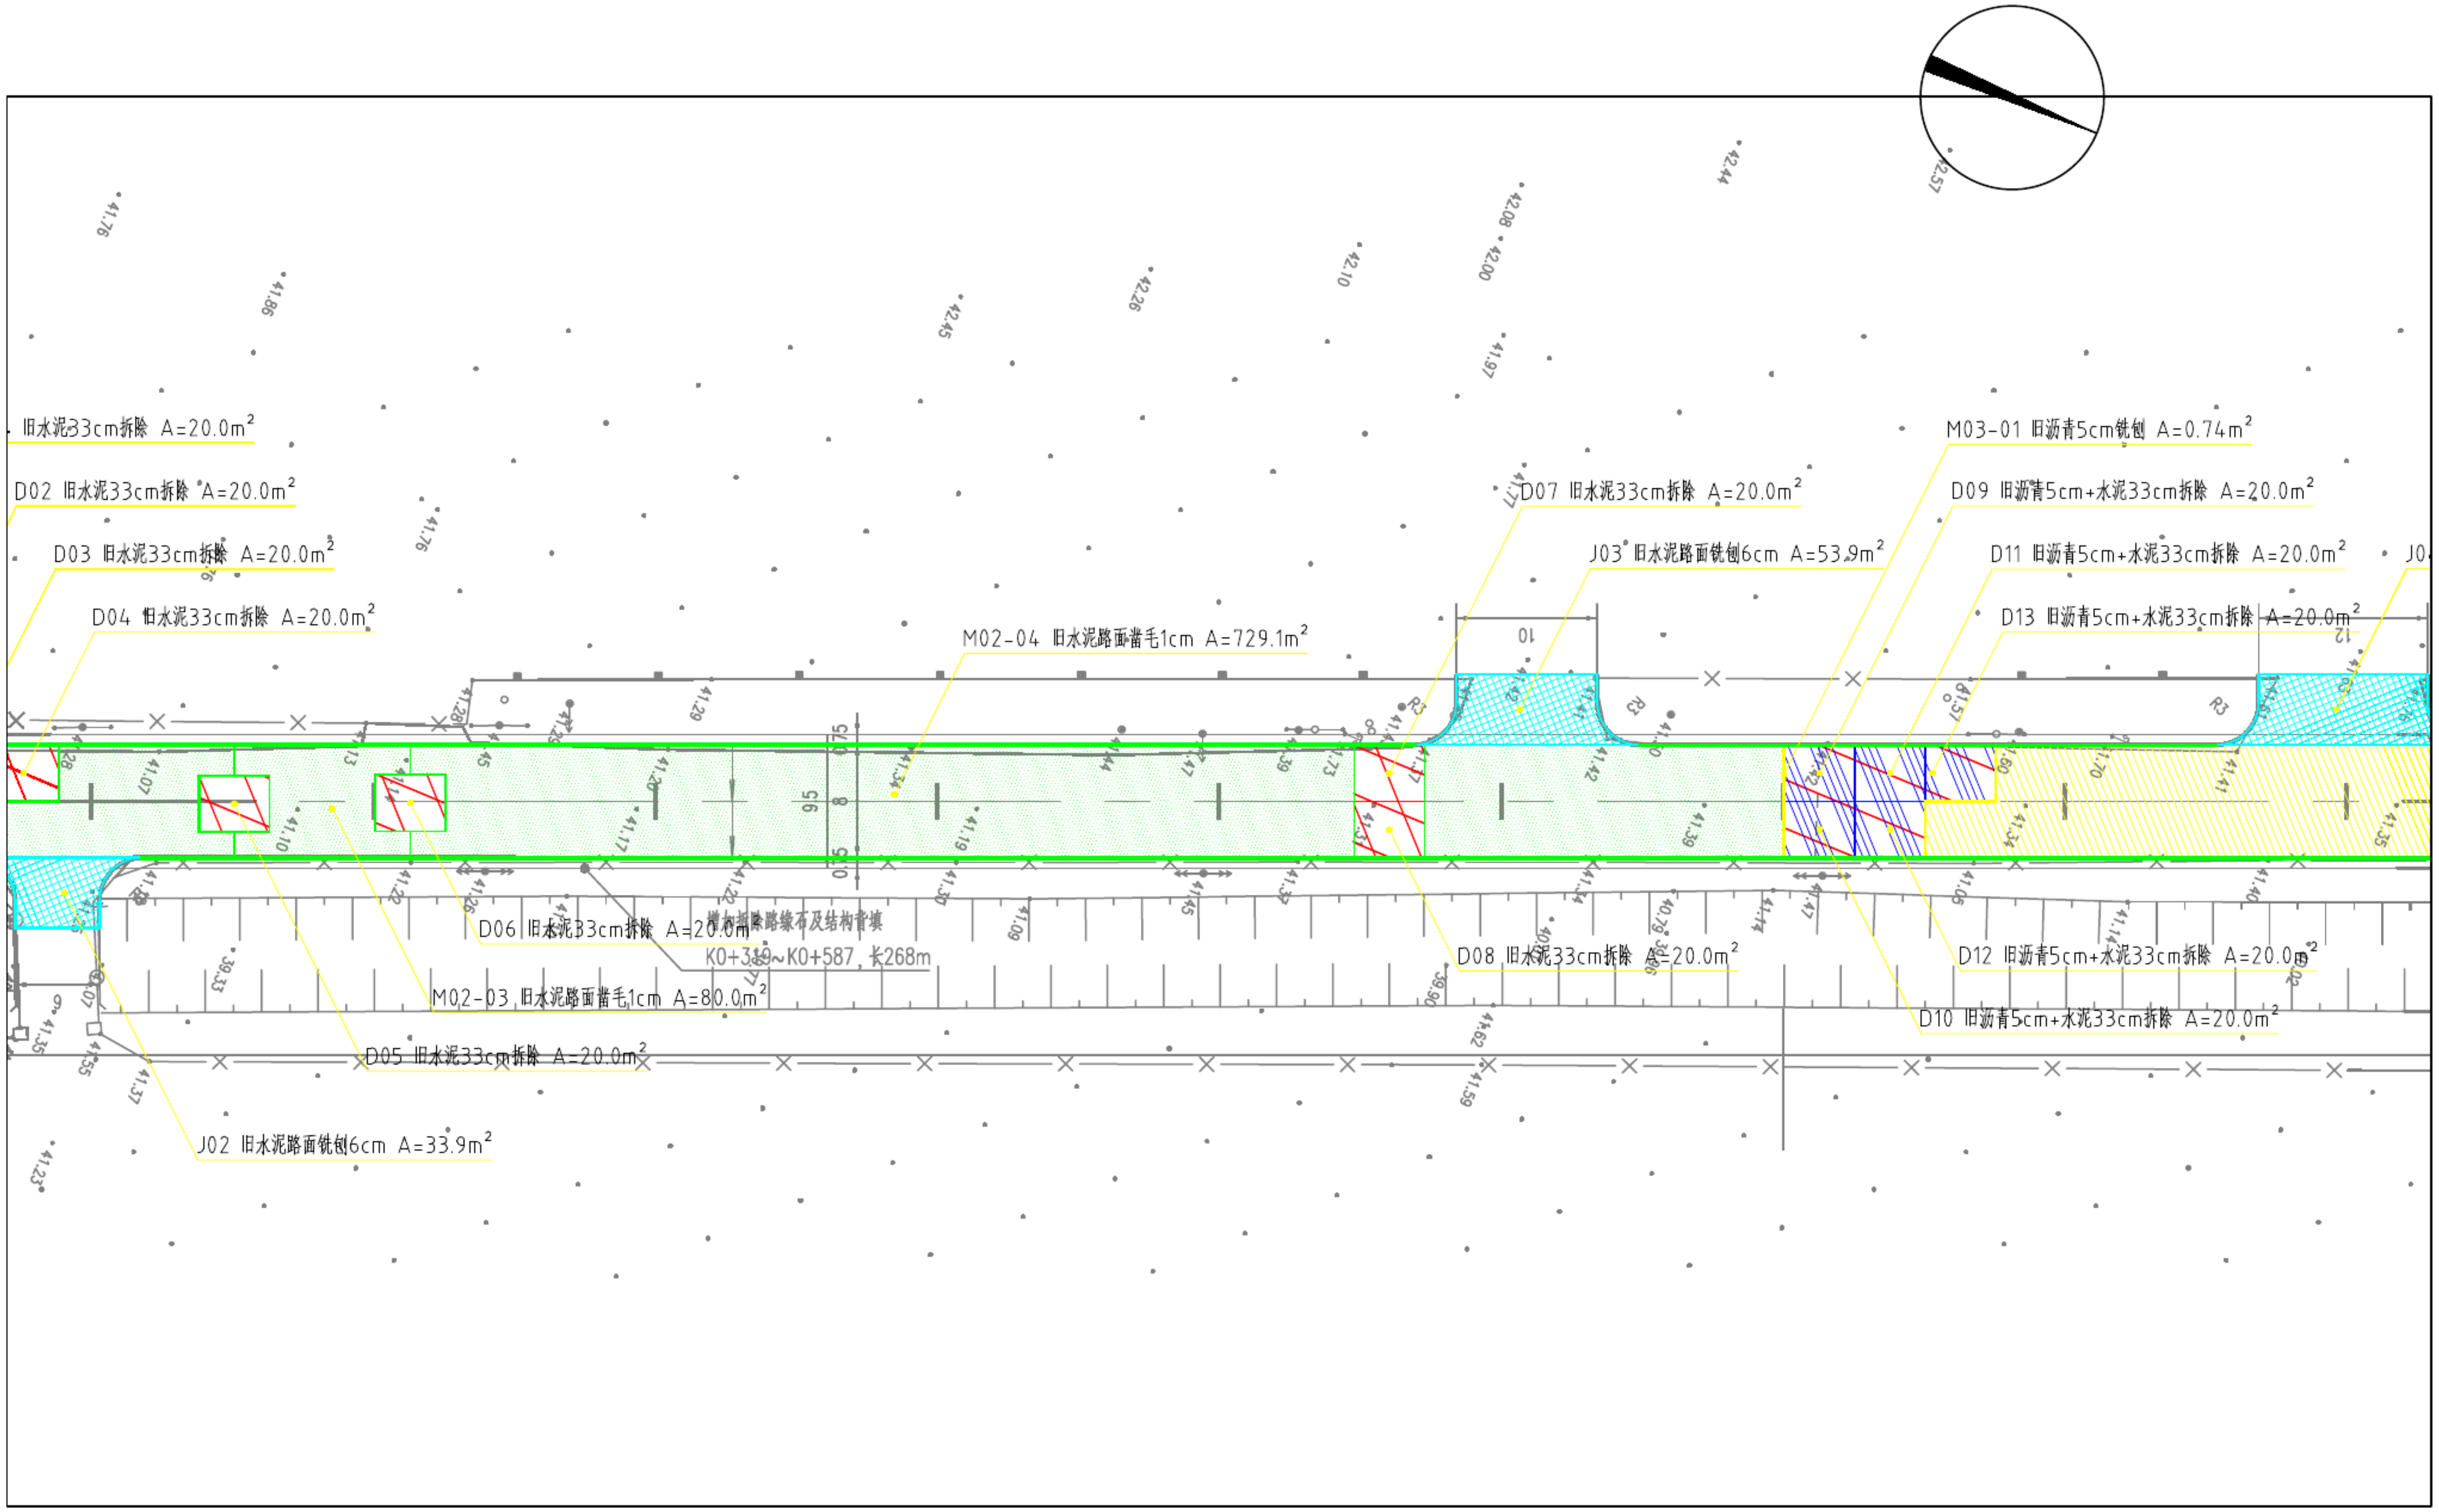
旧水泥33cm拆除 A=20.0m²
D02 旧水泥33cm拆除 A=20.0m²
D03 旧水泥33cm拆除 A=20.0m²
D04 旧水泥33cm拆除 A=20.0m²
M02-04 旧水泥路面凿毛1cm A=729.1m²
D07 旧水泥33cm拆除 A=20.0m²
J03 旧水泥路面铣刨6cm A=53.9m²
M03-01 旧沥青5cm铣刨 A=0.74m²
D09 旧沥青5cm+水泥33cm拆除 A=20.0m²
D11 旧沥青5cm+水泥33cm拆除 A=20.0m²
D13 旧沥青5cm+水泥33cm拆除 A=20.0m²
J0
10
12
R3
R3
R3
0.75
8
0.5
9.5
D06 旧水泥33cm拆除 A=20.0m²
增加拆除路缘石及结构背填
K0+319~K0+587，长268m
M02-03 旧水泥路面凿毛1cm A=80.0m²
D05 旧水泥33cm拆除 A=20.0m²
J02 旧水泥路面铣刨6cm A=33.9m²
D08 旧水泥33cm拆除 A=20.0m²
D12 旧沥青5cm+水泥33cm拆除 A=20.0m²
D10 旧沥青5cm+水泥33cm拆除 A=20.0m²

▨ 旧沥青5cm铣刨

▨ 旧水泥路面铣刨6cm

▦ 旧步道砖6cm+基层17cm拆除

旧缘石拆除：绿色加粗线

▨ 旧沥青5cm+水泥33cm拆除

▨ 旧水泥路面凿毛1cm

▨ 旧水泥33cm拆除

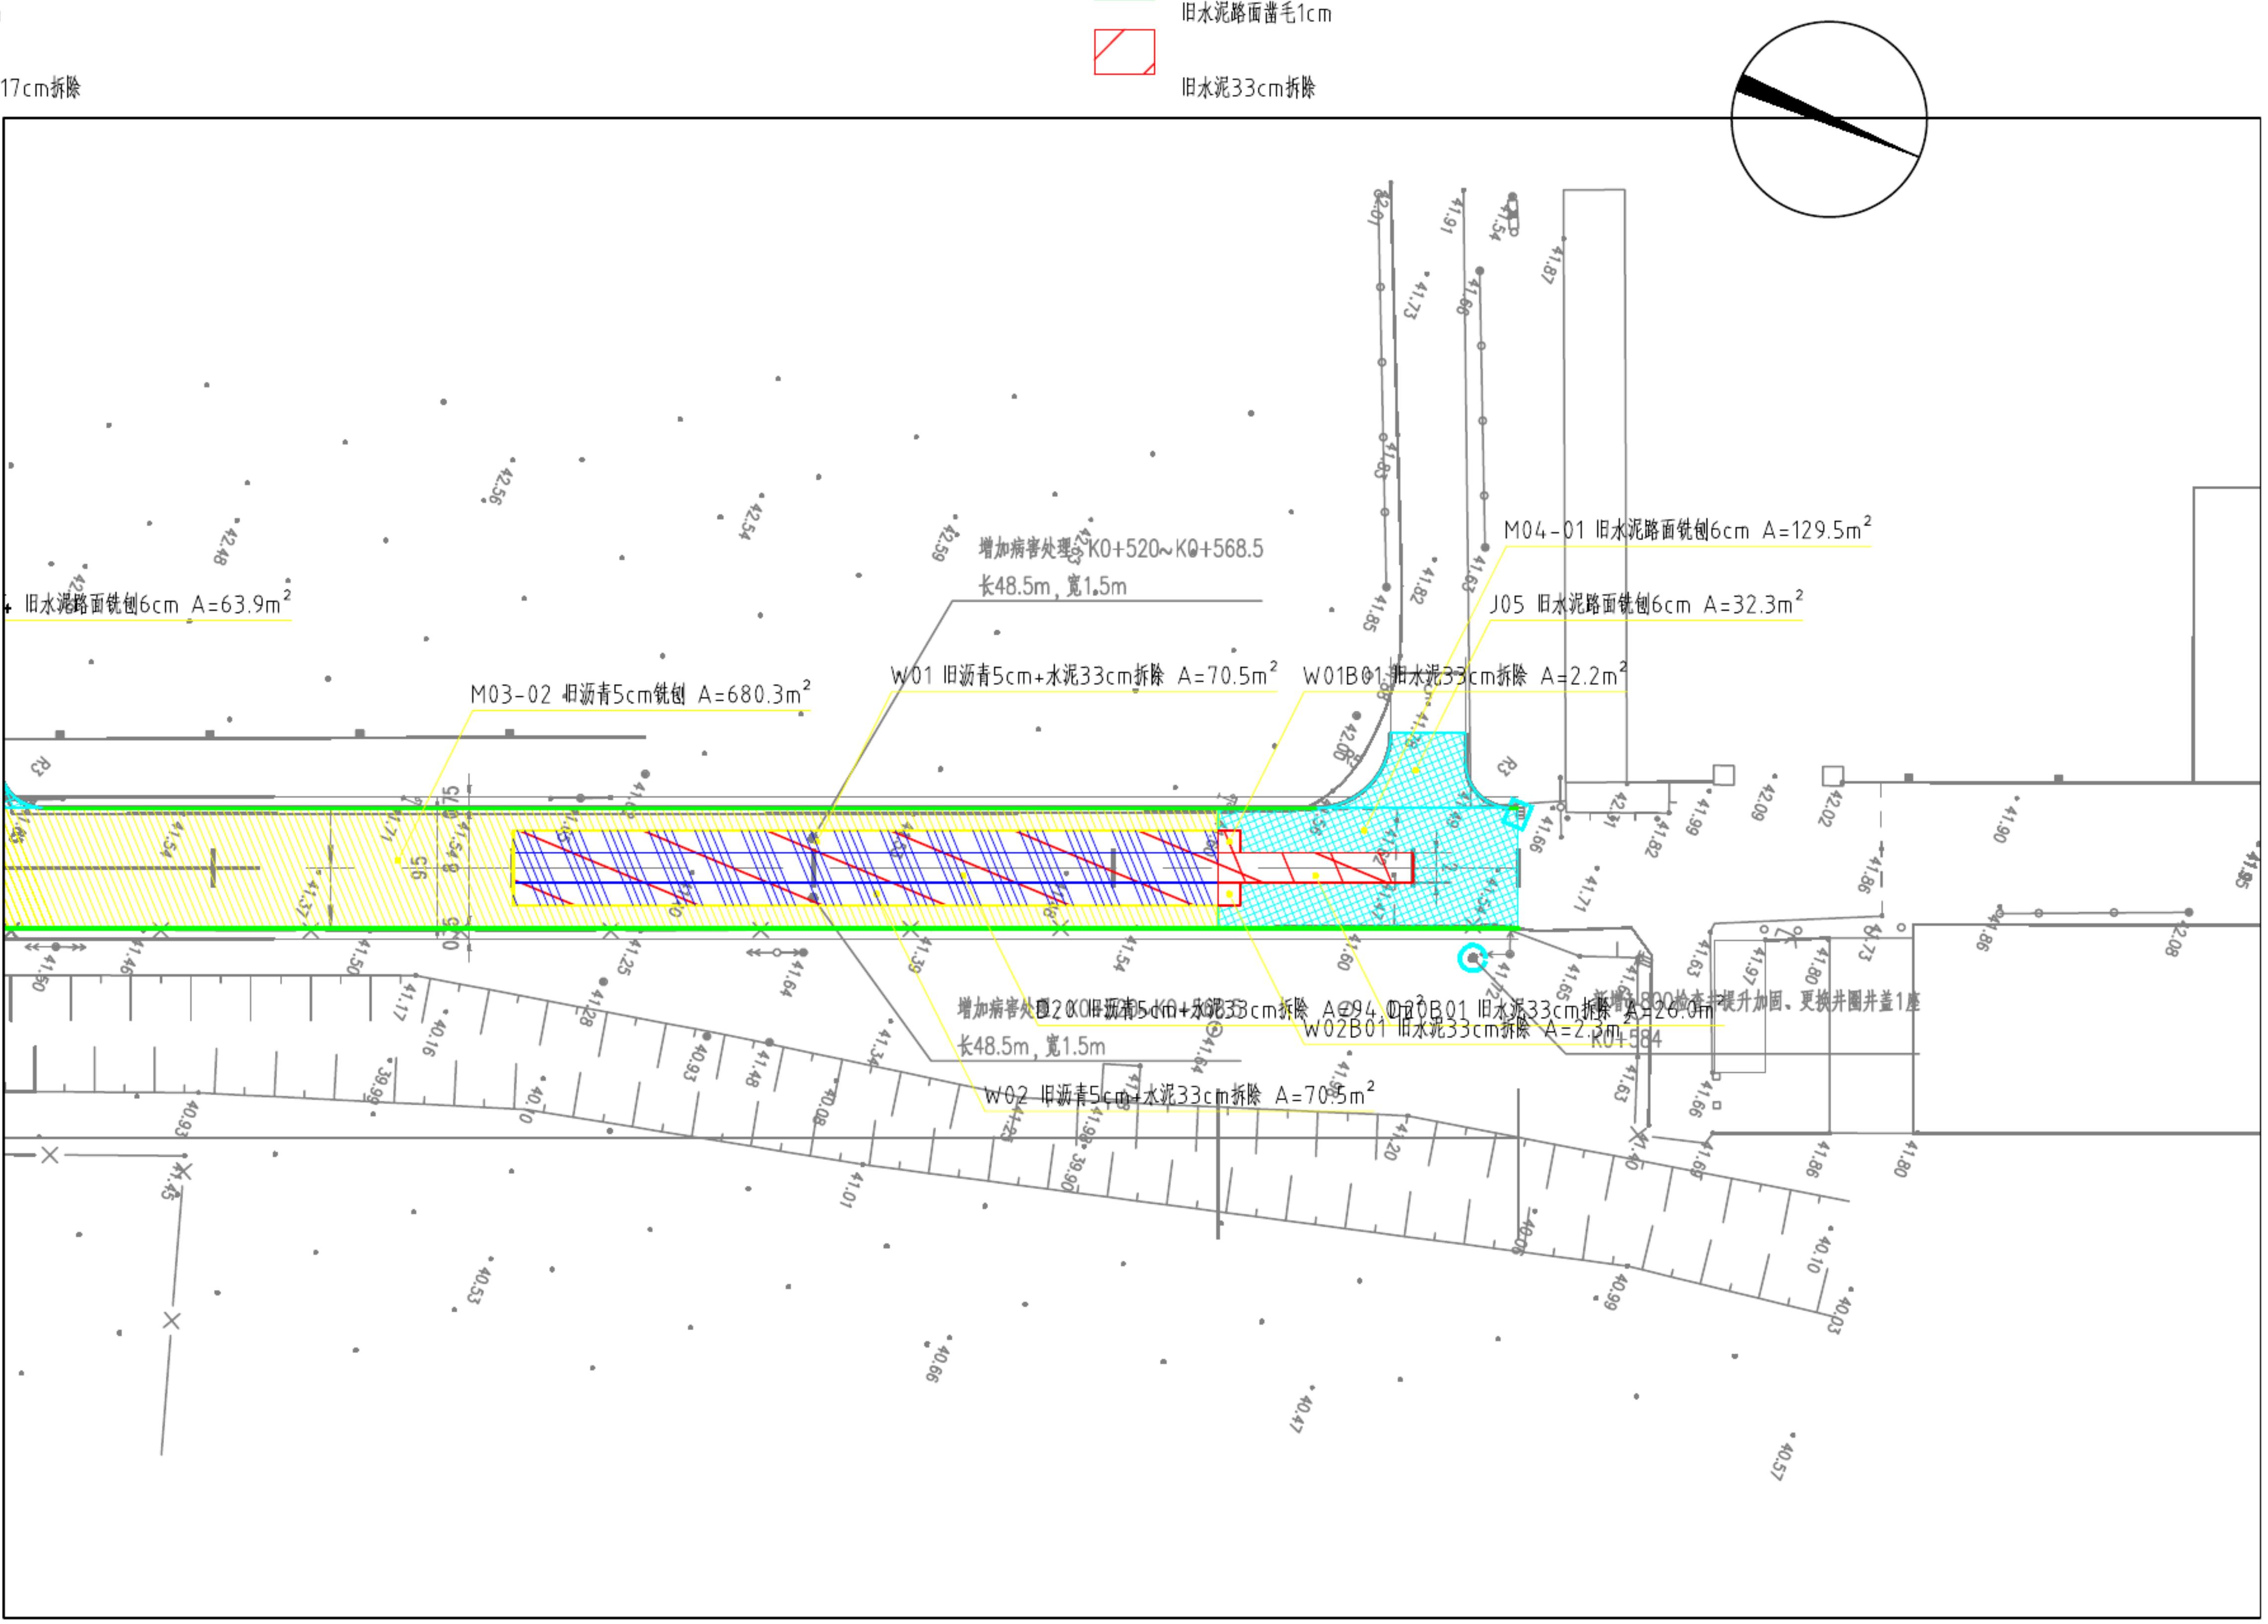

旧水泥路面铣刨6cm A=63.9m²
M03-02 旧沥青5cm铣刨 A=680.3m²
增加病害处理：K0+520~K0+568.5
长48.5m，宽1.5m
W01 旧沥青5cm+水泥33cm拆除 A=70.5m²
W01B01 旧水泥33cm拆除 A=2.2m²
M04-01 旧水泥路面铣刨6cm A=129.5m²
J05 旧水泥路面铣刨6cm A=32.3m²
增加病害处理：K0+520~K0+568.5
长48.5m，宽1.5m
D20 旧沥青5cm+水泥33cm拆除 A=94.0m²
D20B01 旧水泥33cm拆除 A=26.0m²
W02B01 旧水泥33cm拆除 A=2.3m²
新增Φ800检查井提升加固、更换井圈井盖1座
K0+584
W02 旧沥青5cm+水泥33cm拆除 A=70.5m²
R3
R3