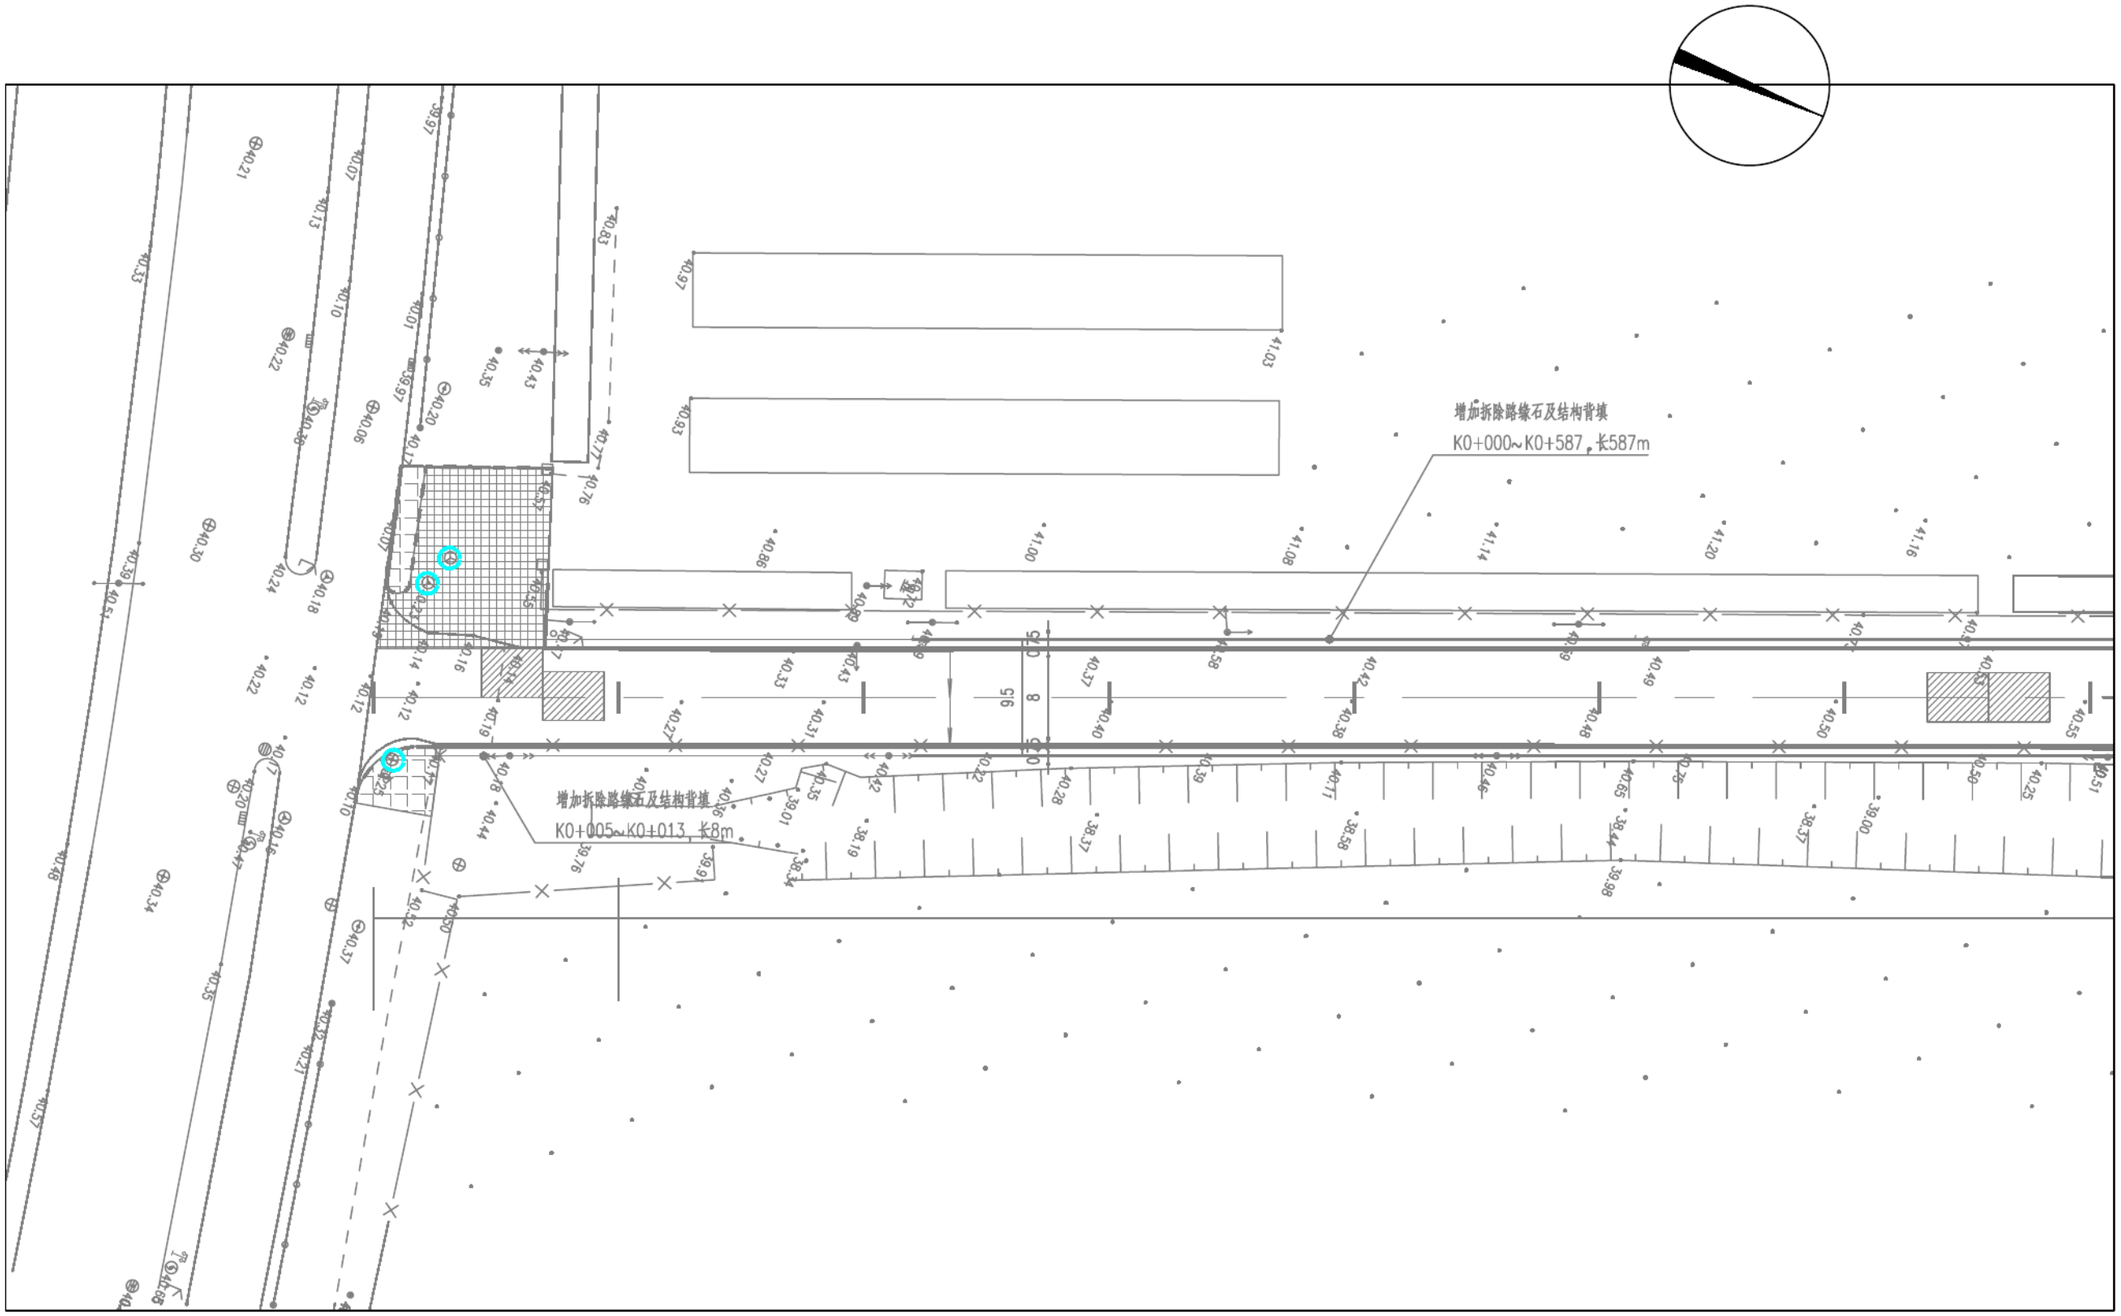
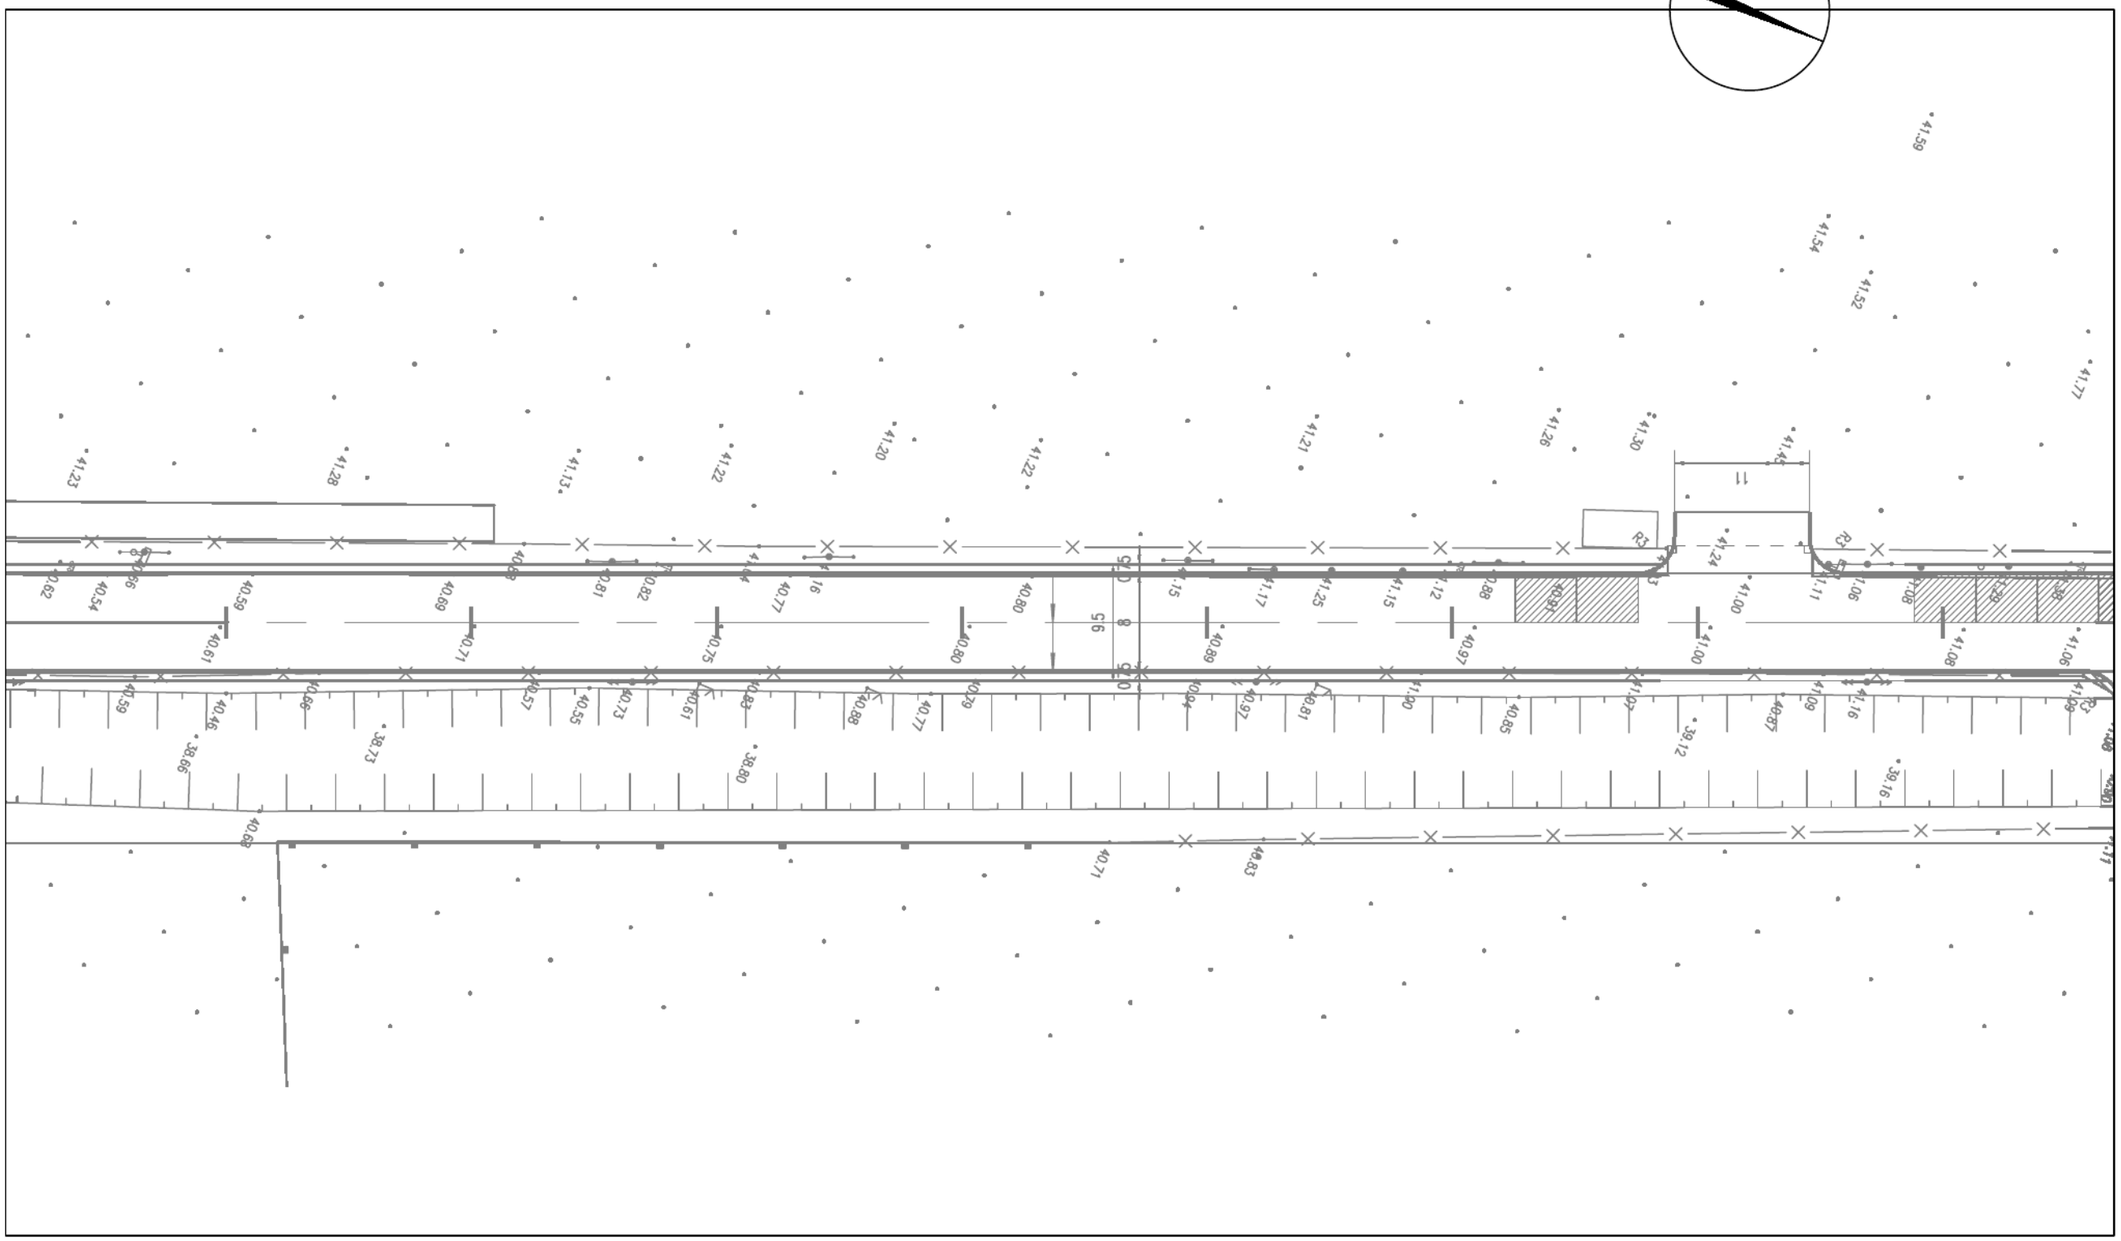
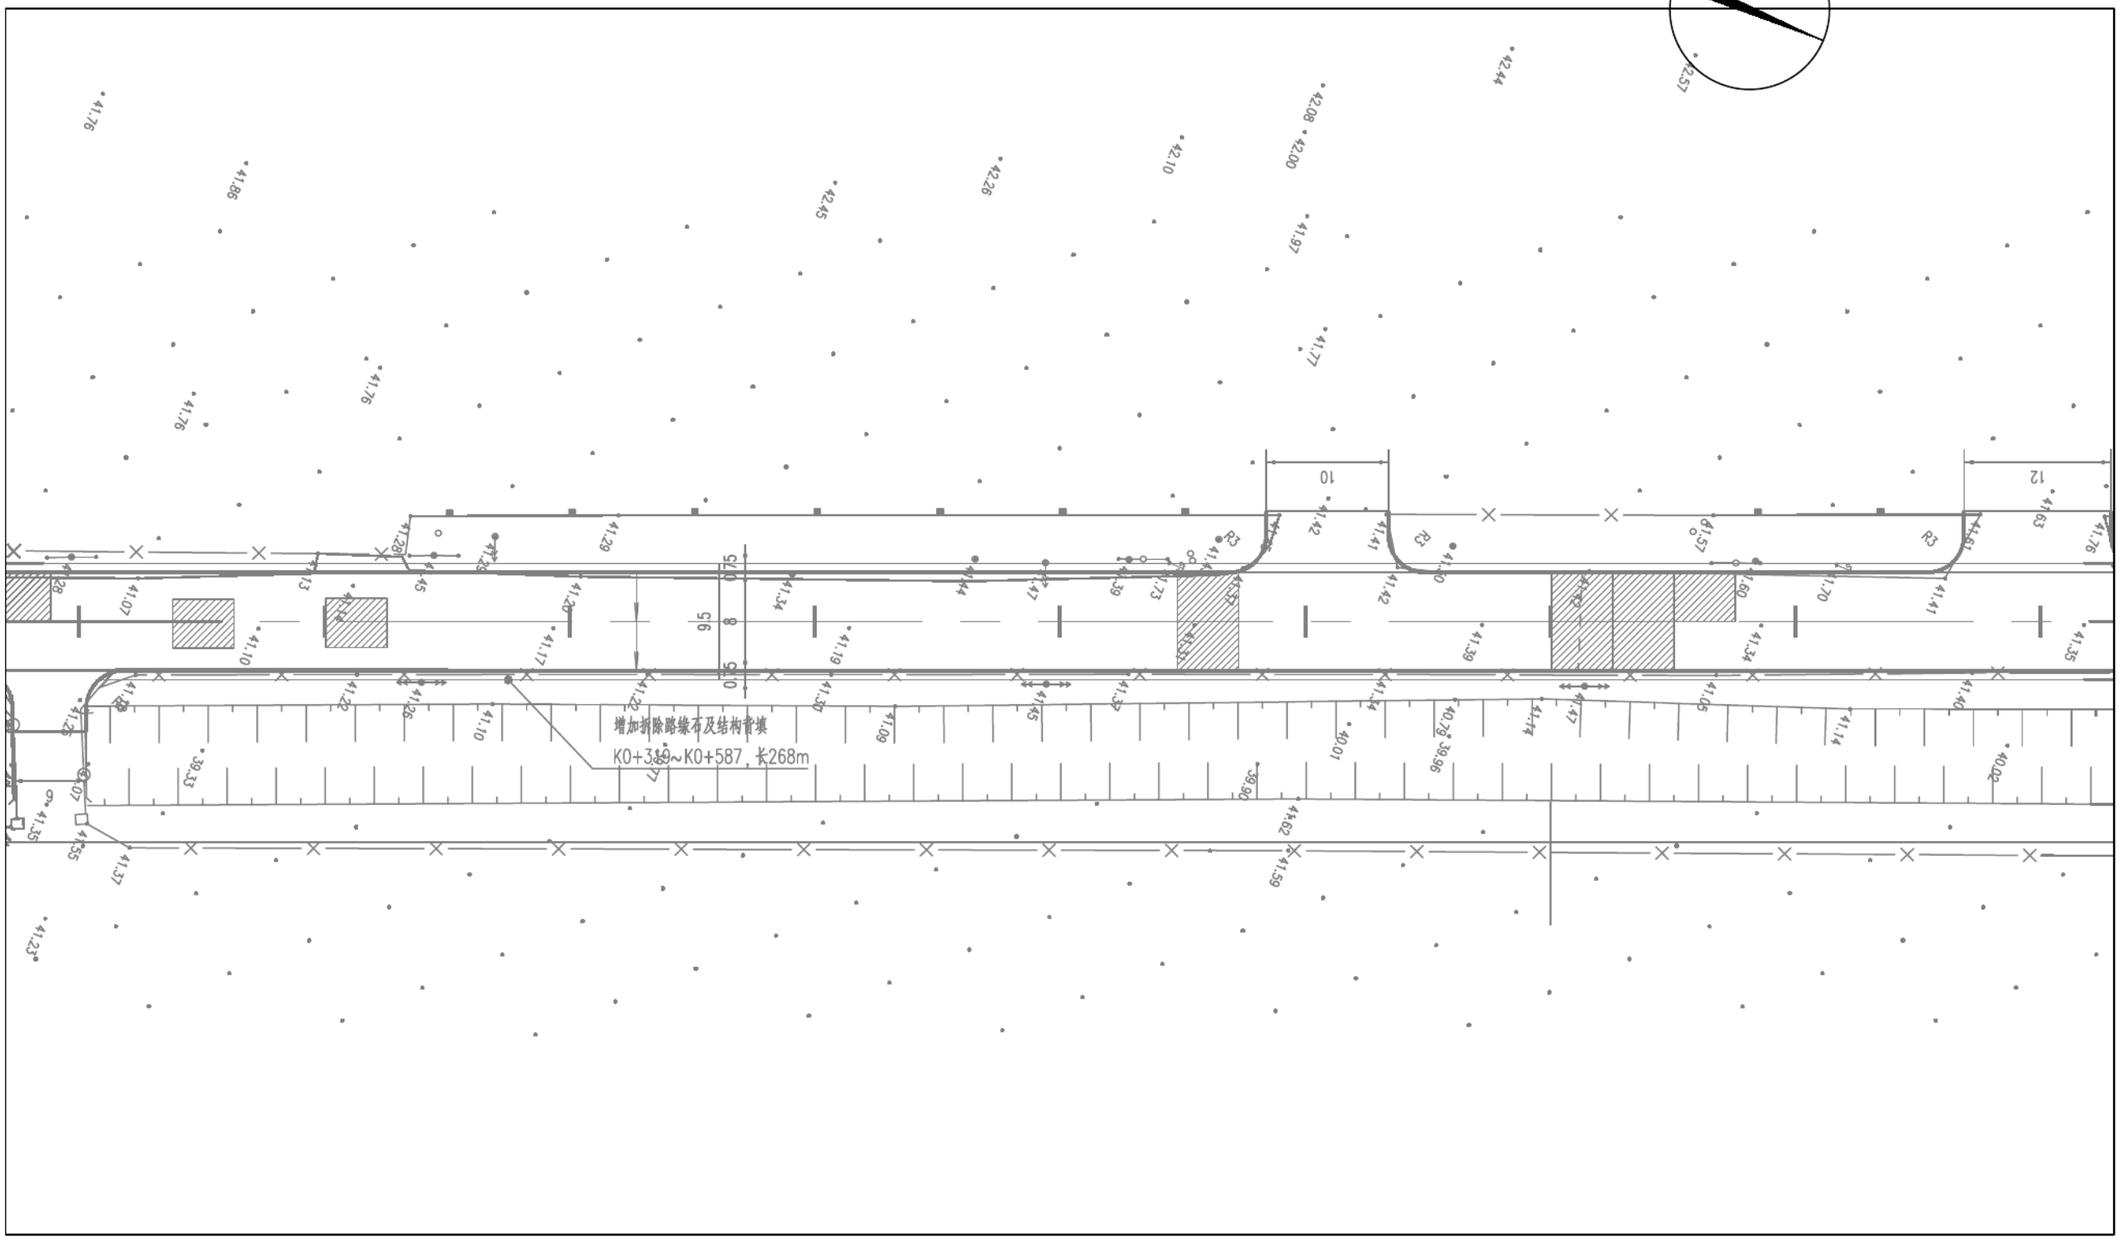
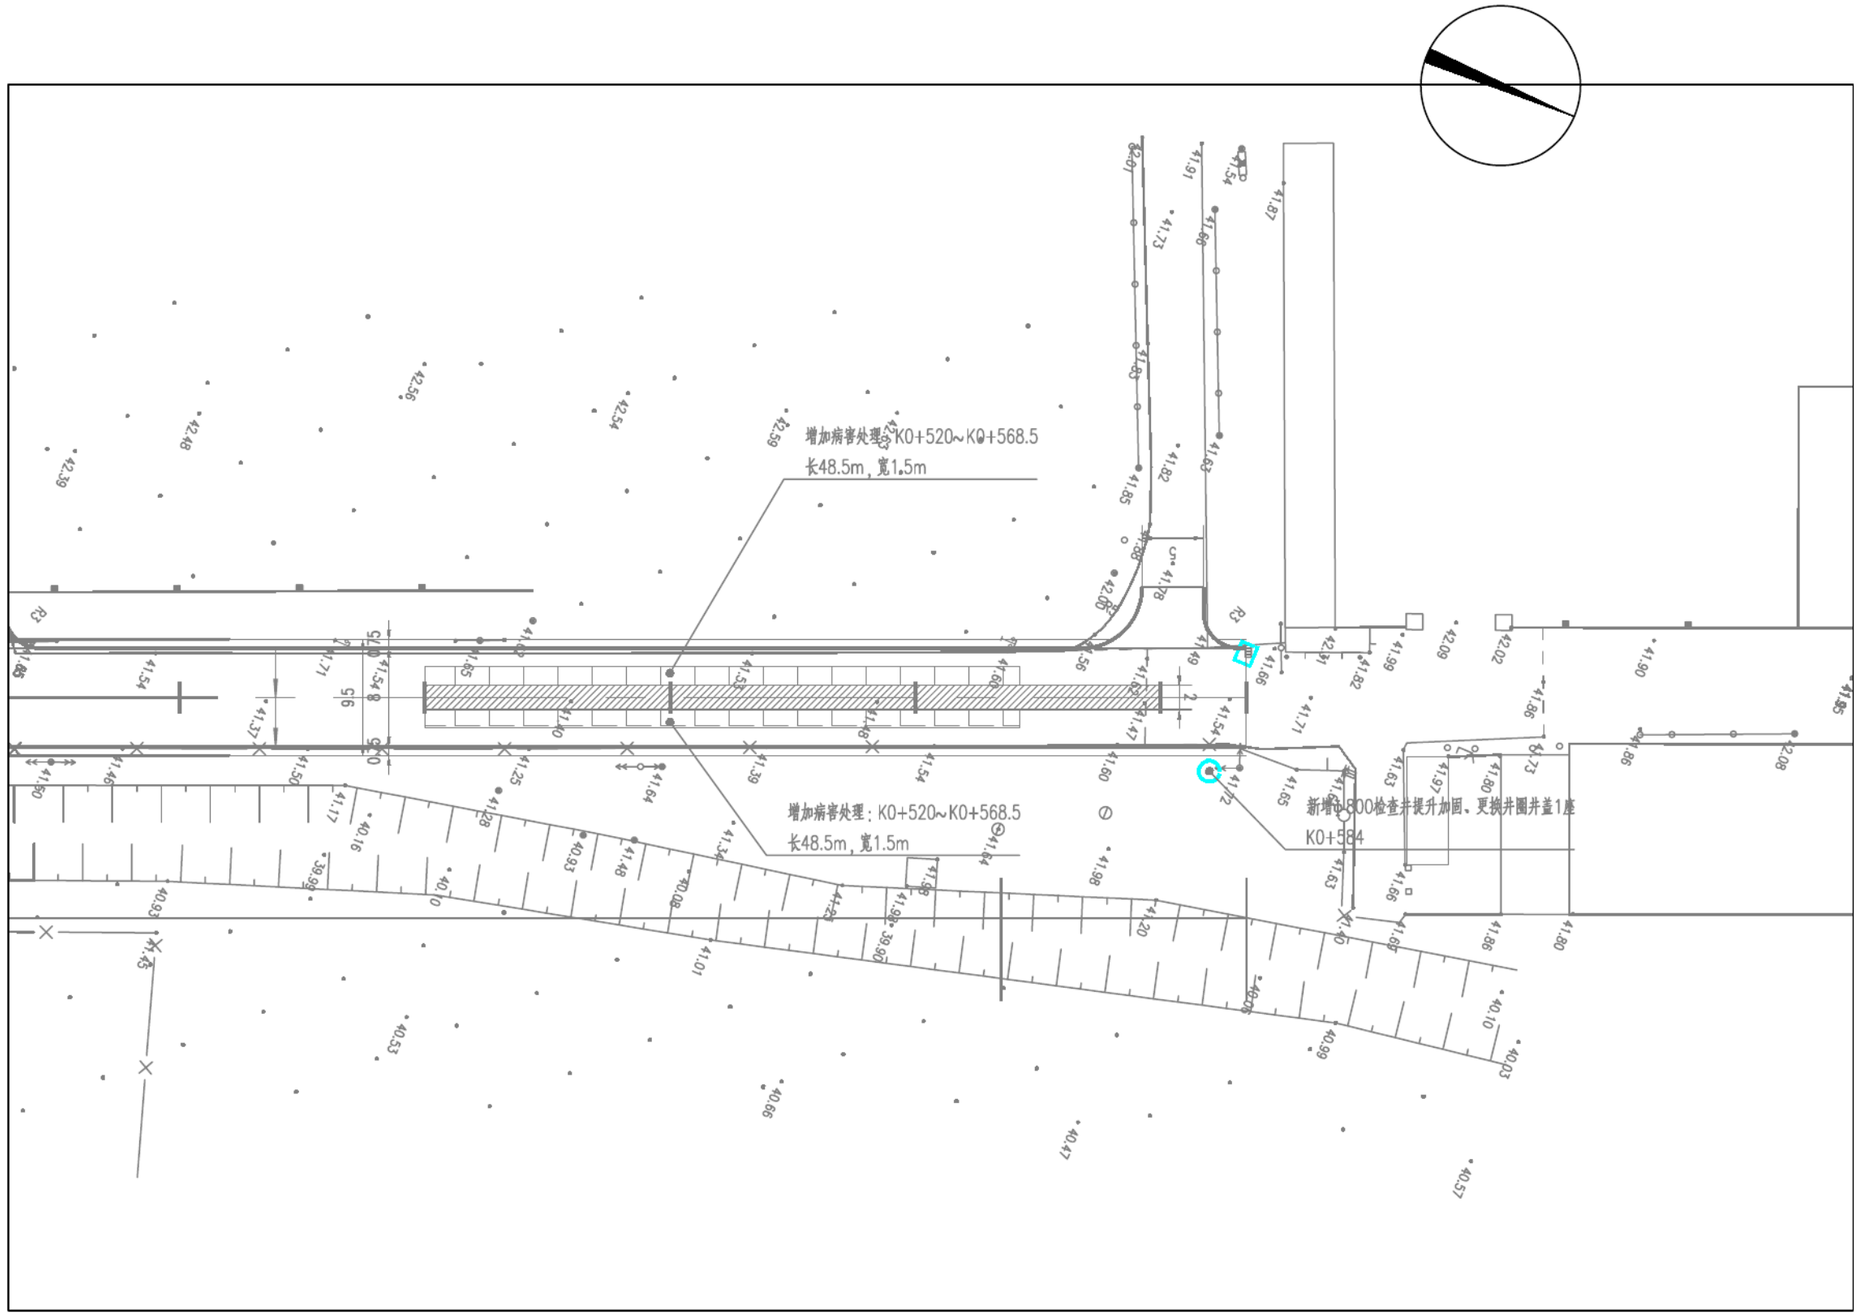

增加拆除路缘石及结构背填
K0+000~K0+587，长587m
增加拆除路缘石及结构背填
K0+005~K0+013，长8m




增加拆除路缘石及结构背填
K0+319～K0+587，长268m


增加病害处理：K0+520~K0+568.5
长48.5m，宽1.5m
增加病害处理：K0+520~K0+568.5
长48.5m，宽1.5m
新增Φ800检查井提升加固、更换井圈井盖1座
K0+584